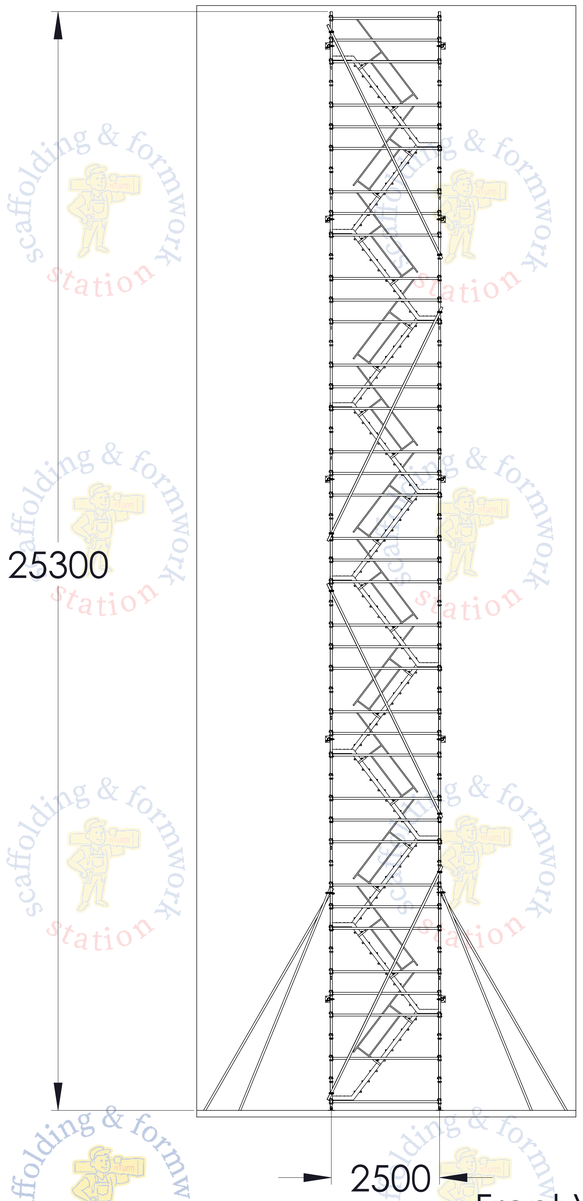

Front View

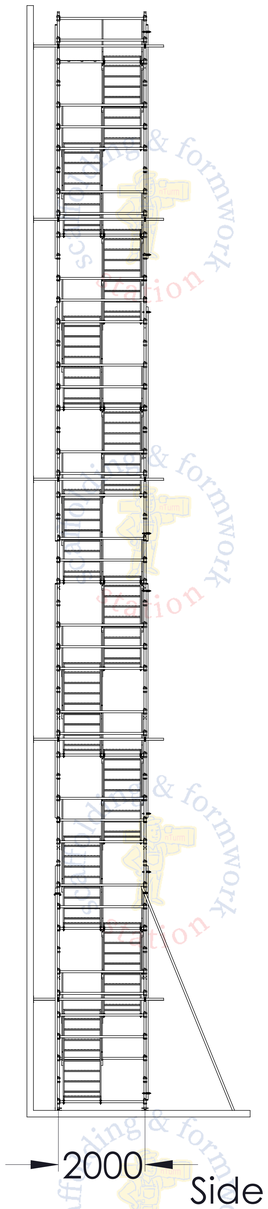

Side View

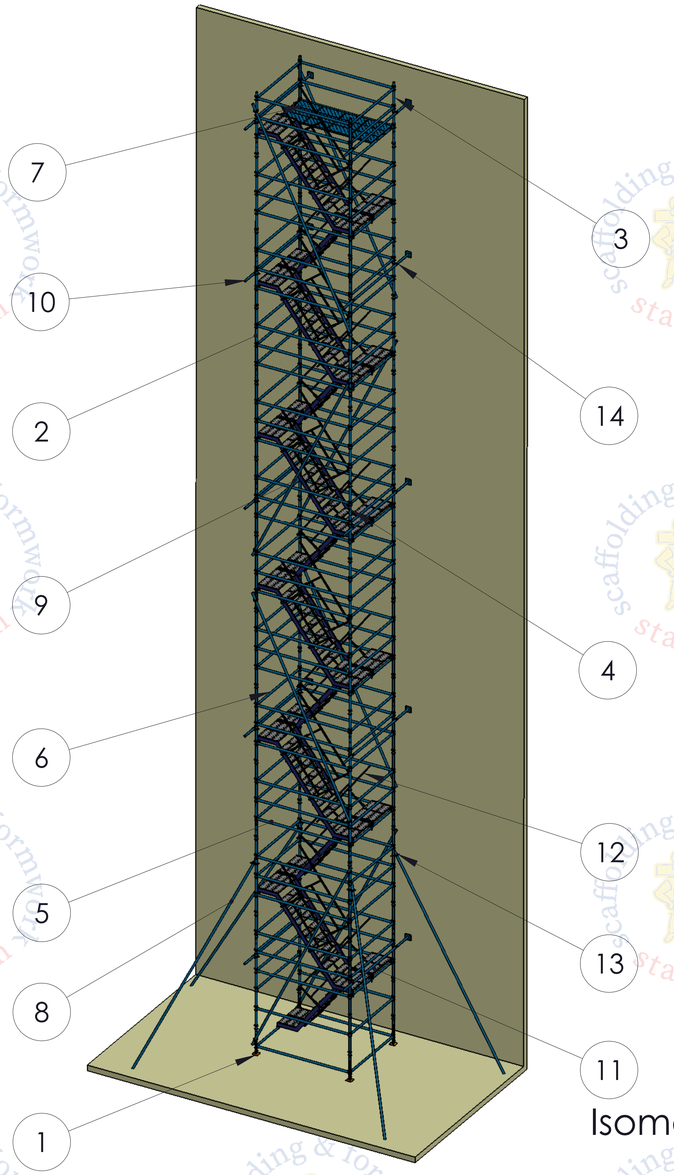

Isometric View

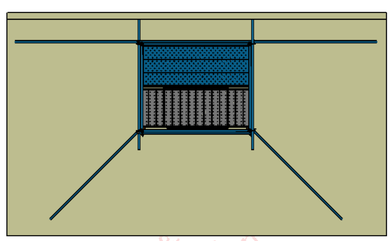

Top View

SCALE :1:50	A0

UNLESS OTHERWISE SPECIFIED ALL DIMENSIONS ARE IN MM

TITLE : **Cuplock Tower 2.5x2x25.3 Mtr**

Dwg. No.: CS41A

Page 1/1

	NAME	DATE
DRAWN	SKS	29/01/25
CHK'D		
APPV'D	ABY	

MATERIAL : MS

nTurm
Your Safety is Our Priority

Tower Specification	
Scaffold Dimensions	2.5x2x25.3Mtr
Working Height	26 Mtr
Tower Height	25.3 Mtr
Platform Height	24 Mtr
Bay size	2.5x2 Mtr

S. No.	BOQ List	QTY.
1	Base Jack Solid 400 mm	4
2	Cuplock Vertical 3 Mtr with 6 Cups	32
3	Cuplock Vertical 1.3 Mtr with 3 Cups	4
4	Spigot 300 mm with double G Lock Pin	32
5	Cuplock Ledger 2.5 Mtr	76
6	Cuplock Ledger 2 Mtr	76
7	Antiskid Platform 2.5Lx0.3W Mtr	3
8	Stabilizer 6 Mtr	4
9	Bracing Pipe 6 Mtr	8
10	Anchor with plate 3 Mtr	10
11	MS Staircase 2.5Lx0.825Wx2H with attached Landing	12
12	MS Staircase Handrail 2 Mtr	24
13	Swivel Forged Coupler	28
14	Fixed Forged Coupler	20

scaffolding & formwork station