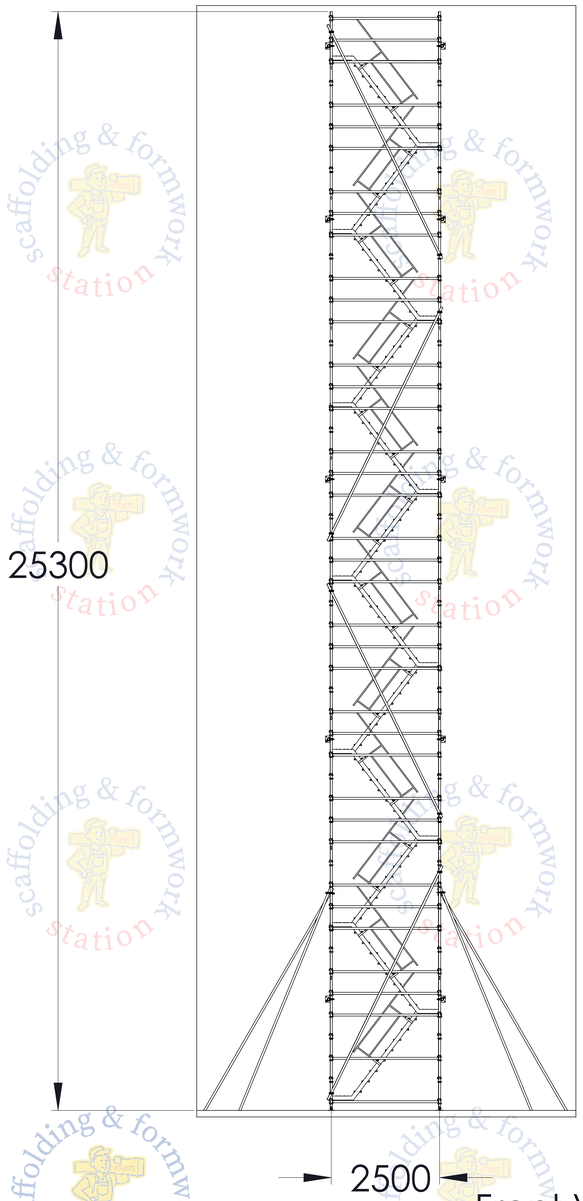

Front View

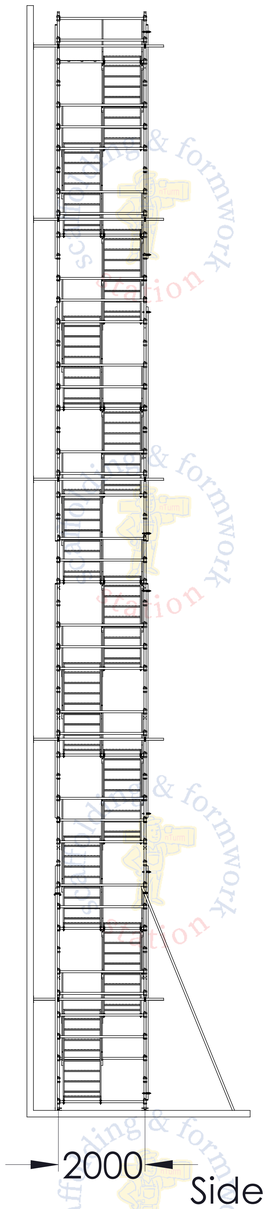

Side View

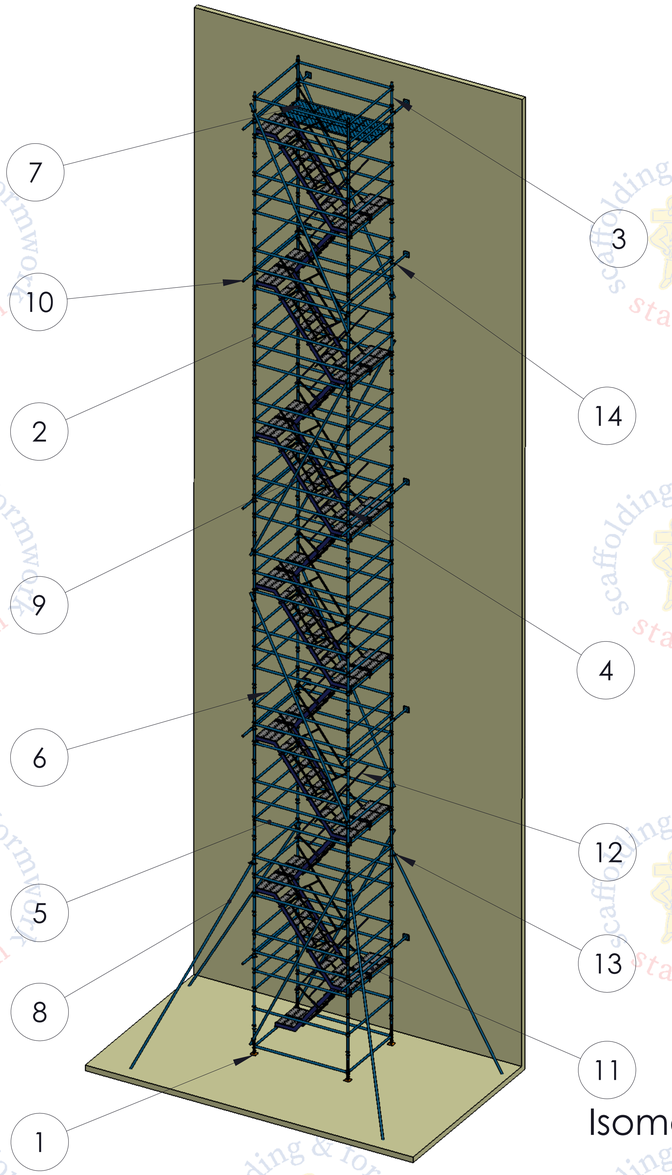

Isometric View

SCALE :1:50	A0

UNLESS OTHERWISE SPECIFIED ALL DIMENSIONS ARE IN MM

TITLE : **Cuplock Tower 2.5x2x25.3 Mtr**

Dwg. No.: CS41A

Page 1/1

[redacted]

	NAME	DATE
DRAWN	SKS	29/01/25
CHK'D		
APPV'D	ABY	

MATERIAL : MS

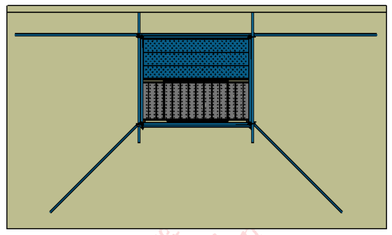

Top View

Tower Specification	
Scaffold Dimensions	2.5x2x25.3Mtr
Working Height	26 Mtr
Tower Height	25.3 Mtr
Platform Height	24 Mtr
Bay size	2.5x2 Mtr

S. No.	BOQ List	QTY.
1	Base Jack Solid 400 mm	4
2	Cuplock Vertical 3 Mtr with 6 Cups	32
3	Cuplock Vertical 1.3 Mtr with 3 Cups	4
4	Spigot 300 mm with double G Lock Pin	32
5	Cuplock Ledger 2.5 Mtr	76
6	Cuplock Ledger 2 Mtr	76
7	Antiskid Platform 2.5Lx0.3W Mtr	3
8	Stabilizer 6 Mtr	4
9	Bracing Pipe 6 Mtr	8
10	Anchor with plate 3 Mtr	10
11	MS Staircase 2.5Lx0.825Wx2H with attached Landing	12
12	MS Staircase Handrail 2 Mtr	24
13	Swivel Forged Coupler	28
14	Fixed Forged Coupler	20

scaffolding & formwork station